


AUGER - CAPBRETON

RDC

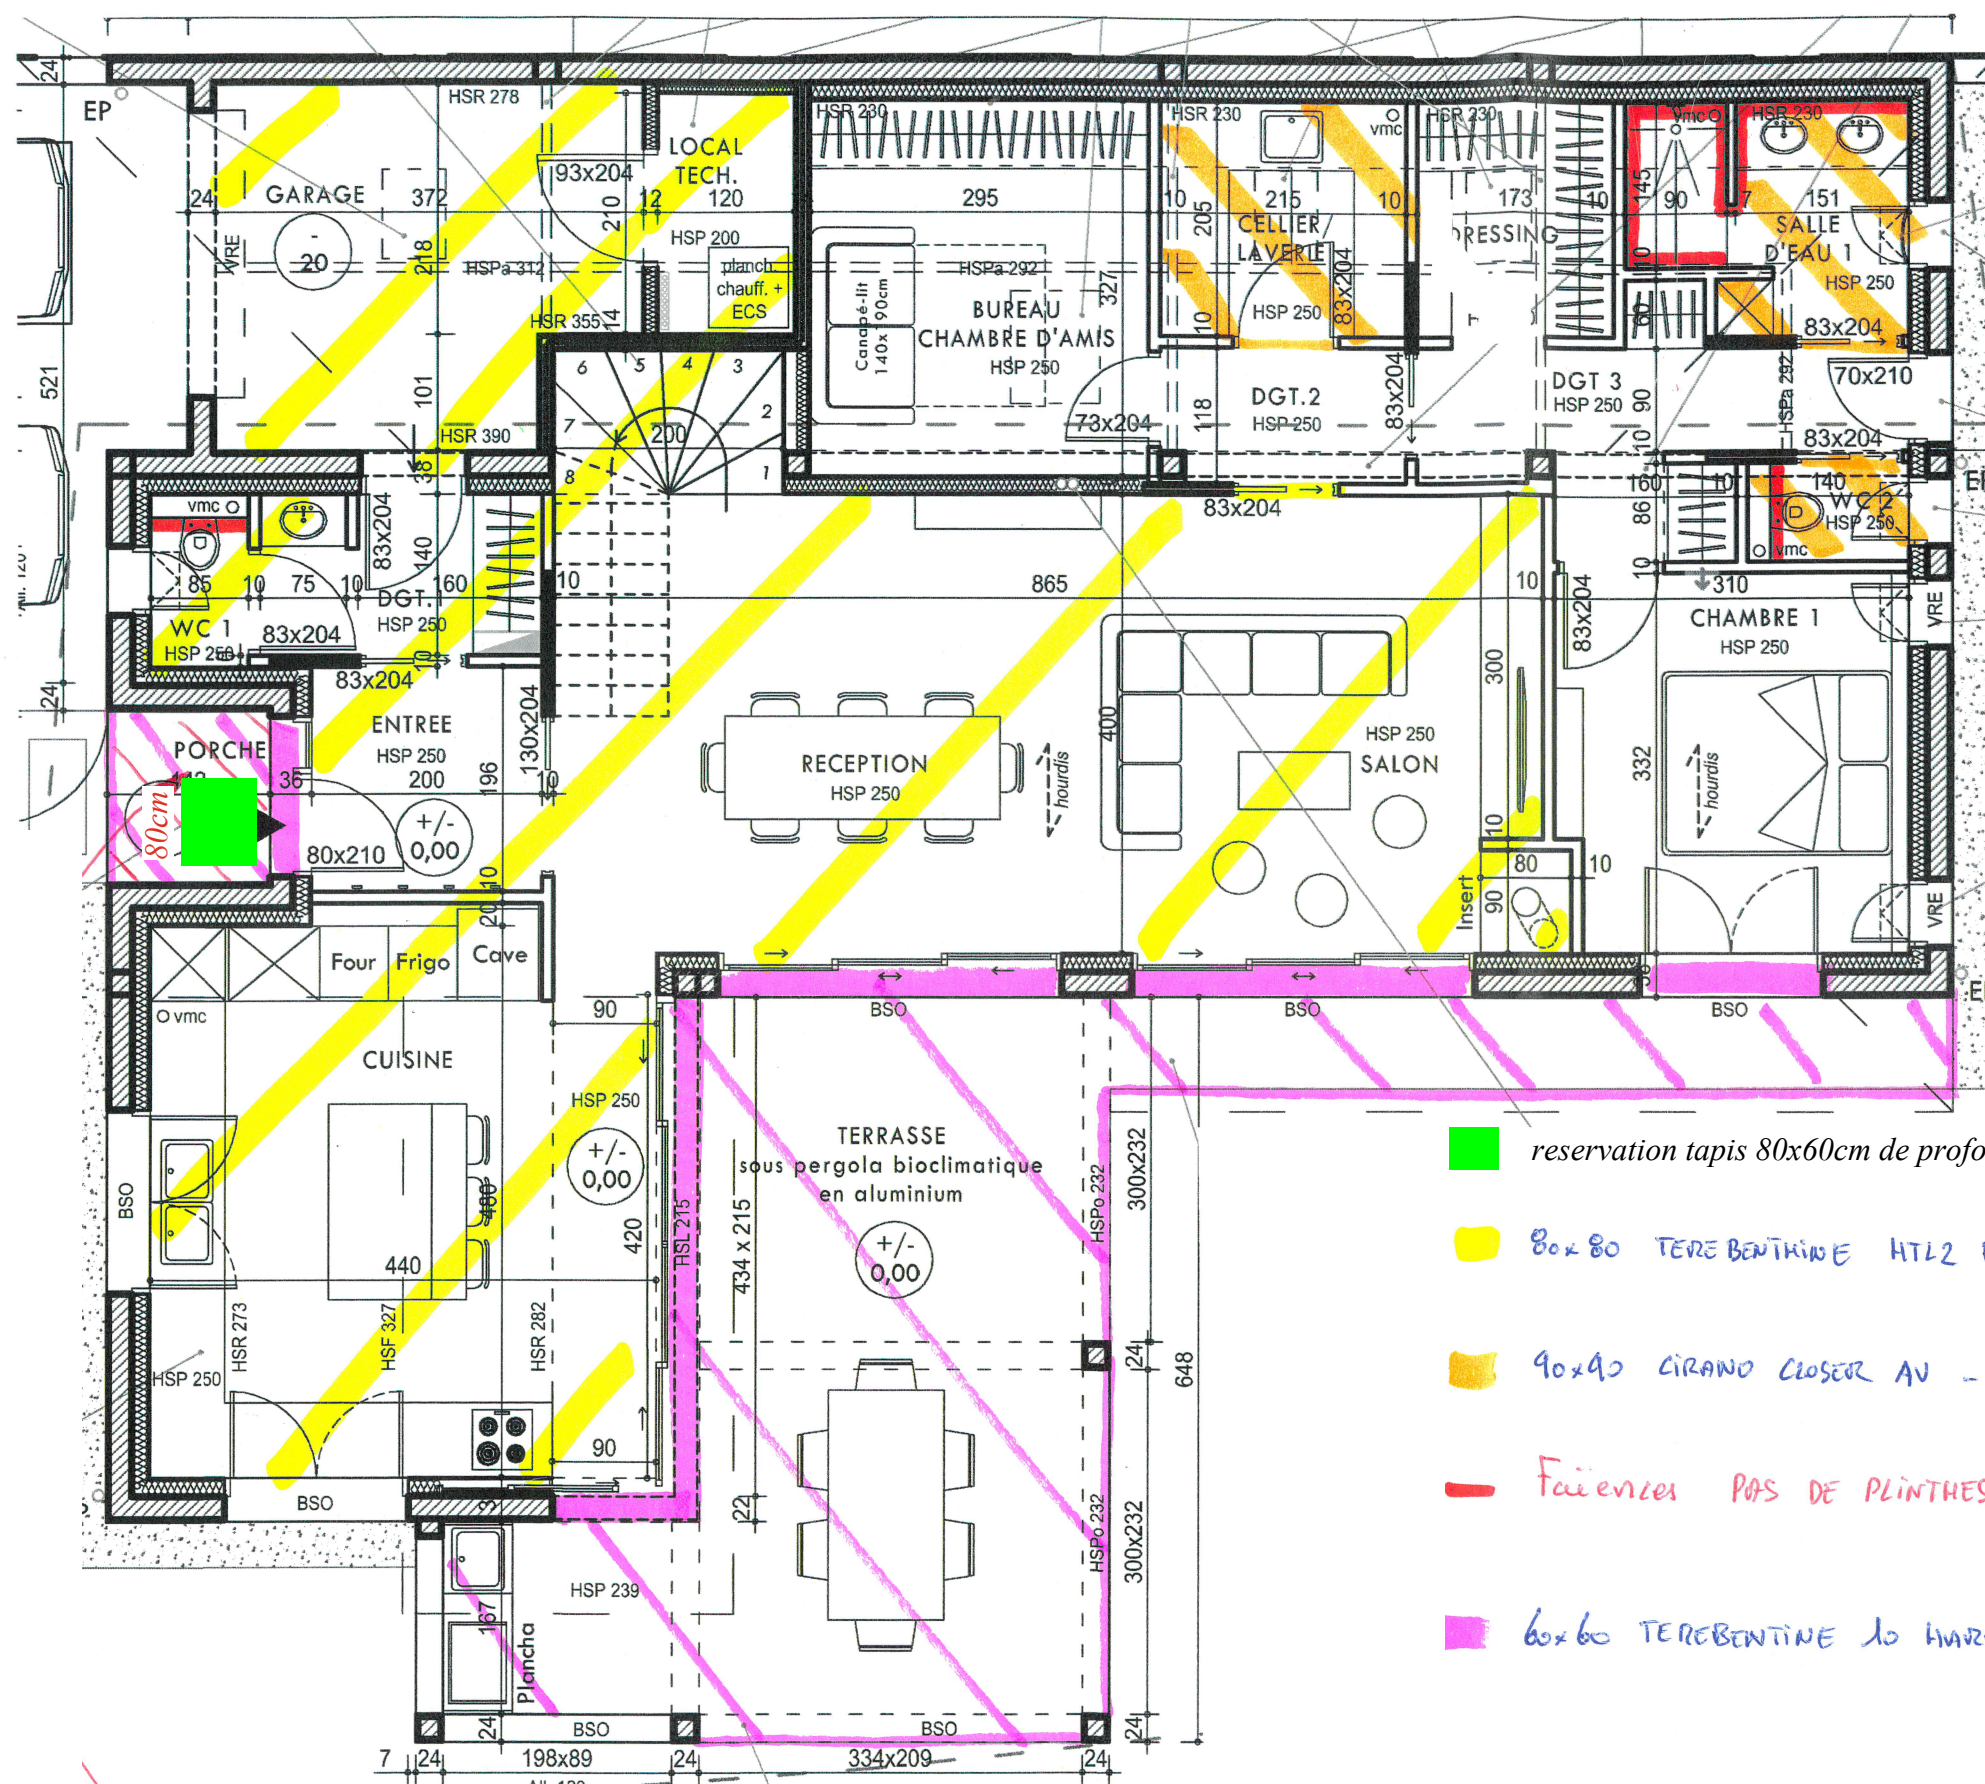


■ reservation tapis 80x60cm de profond devant porte entrée

■ 80x80 TERE BENTHINE HTL2 HARD - joint Dapei 188 + PL (silicone 188)

■ 90x90 CIRANO CLOSER AV - joint Dapei 132 + PL (silicone 132)

— Faïences PAS DE PLINTHES.

■ 60x60 TERE BENTHINE 10 HARD sur plots + Seuls + Retombe terrasses.

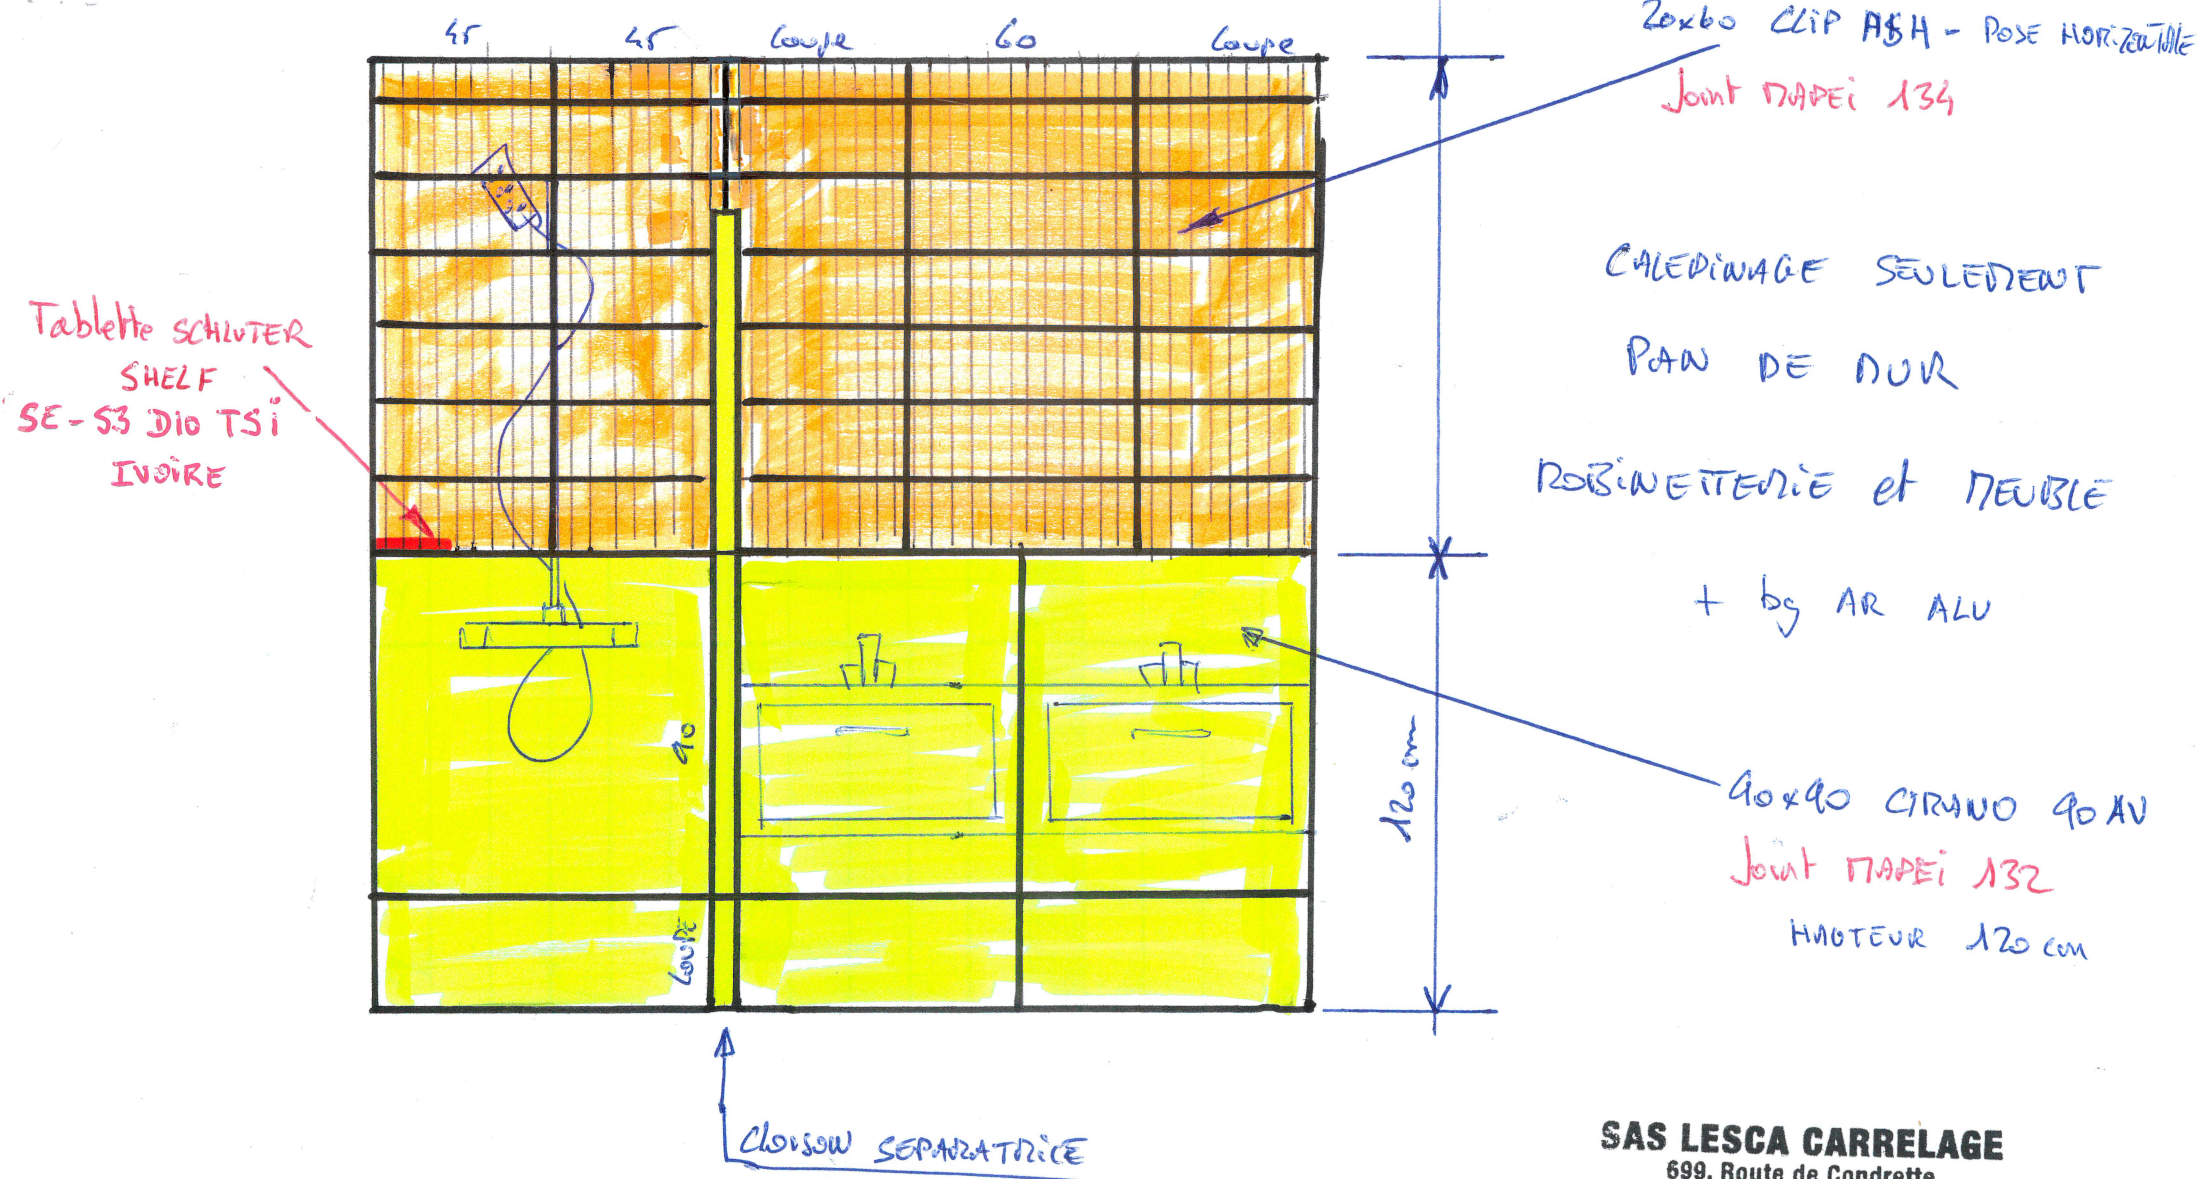

SAS LESCA CARRELAGE
699, Route de Condrette
40400 TARTAS
Tél. : 05 58 73 46 19
Mail : s.lesca@bernadet.net
SIRET : 341 924 546 00011



FUGER
RDC

■ 40x40 CIRANO CLOSER 90 AV
TOUTE HAUTEUR + bg AR ALU
Joint DAPEI 132

— SUIVRE CALEDINAGE ⚠ 02 couleurs joints ⚠
PAN DE DUR ROBINETTERIE et MEUBLE

▨ Tablette SHELF SE S3 D10 TSi à 120 cm du sol
SUIVANT CALEDINAGE

SDE 1

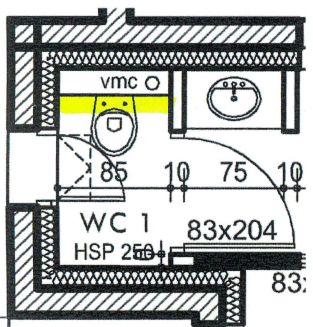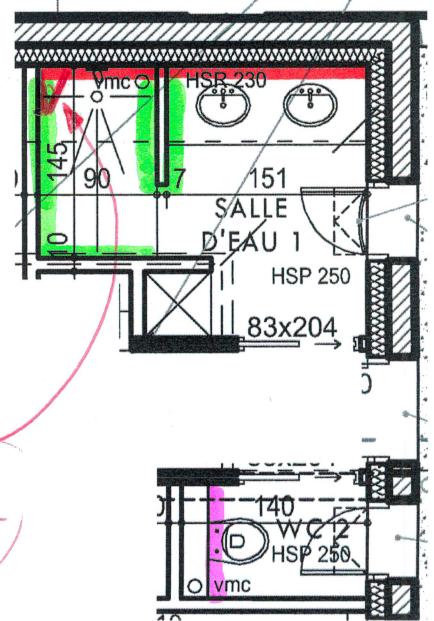

WC 1

■ 80x80 TEREANTHINE HTLZ HARD
Hauteur caisson WC + bg AR ALU
Joint DAPEI 138
Tablette WC en bois

WC 2

■ 60x120 CIRANO TRAITÉ AV
POSE HORIZONTALE Hauteur caisson WC
+ bg AR ALU
Joint DAPEI 132
Tablette WC en bois