


AUGER - CAPBRETON

RDC

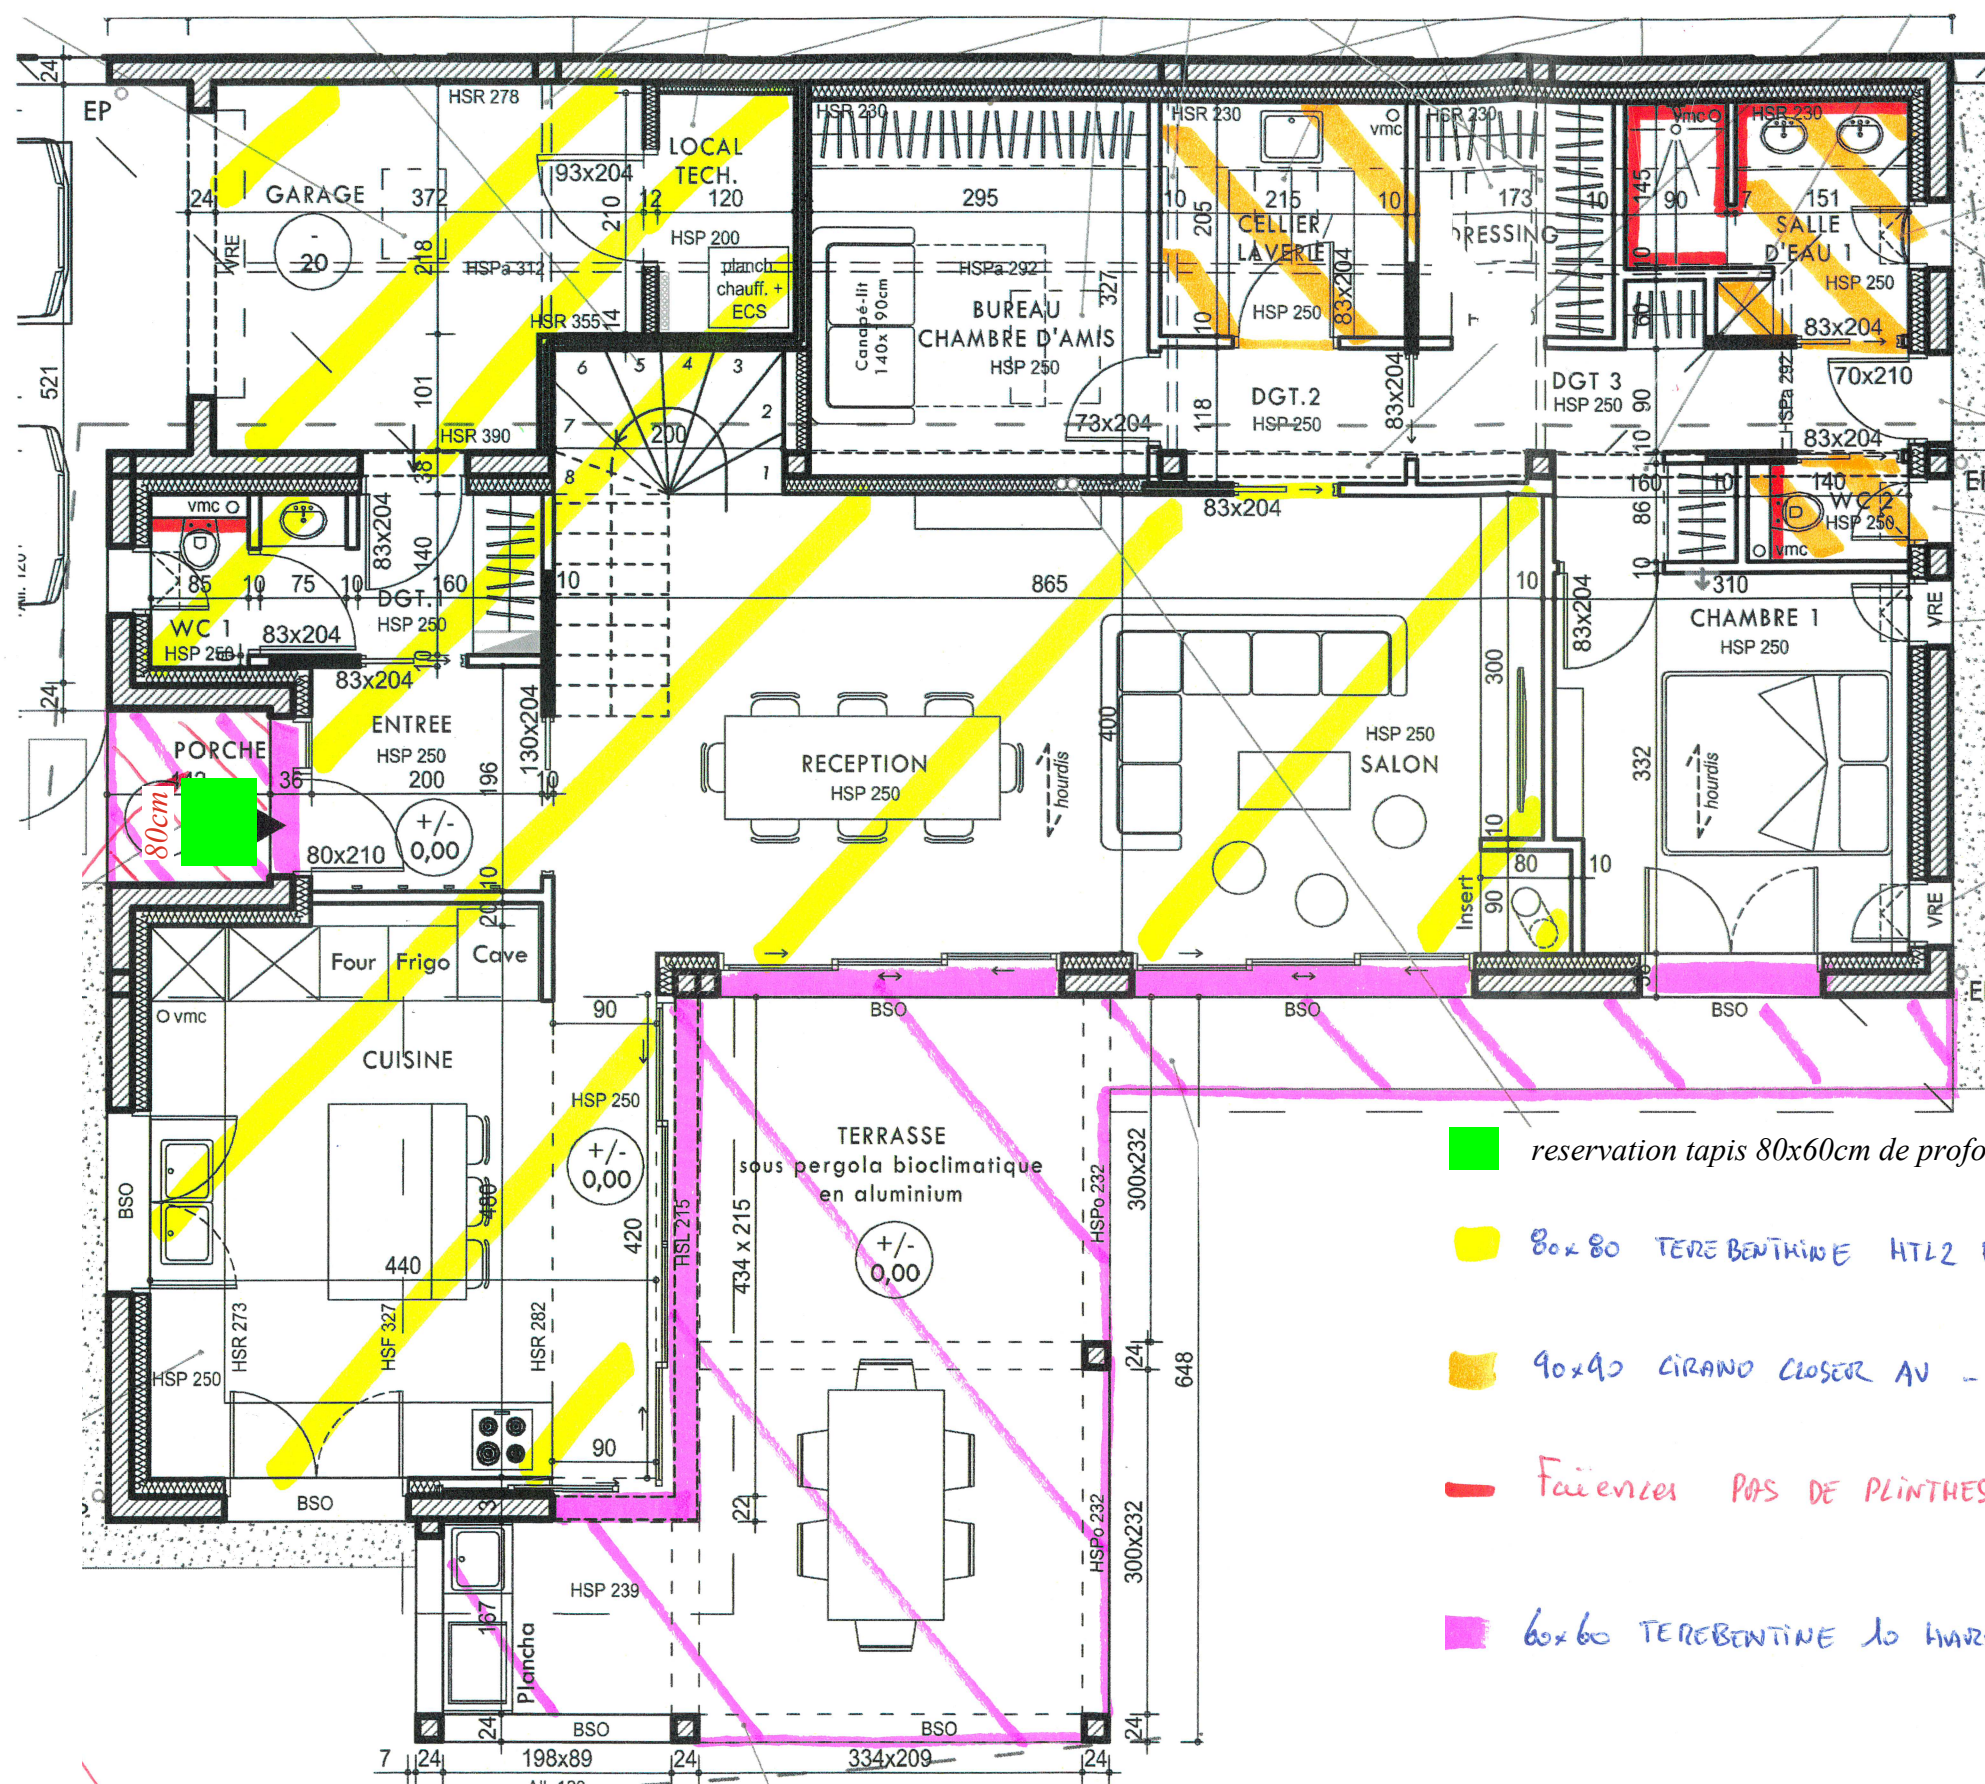

■ reservation tapis 80x60cm de profond devant porte entrée

■ 80x80 TERE BENTHINE HTL2 HARD - joint Dapei 188 + PL (silicone 188)

■ 90x90 CIRANO CLOSER AV - joint Dapei 132 + PL (silicone 132)

— Faïences PAS DE PLINTHES.

■ 60x60 TERE BENTHINE 10 HARD sur plots + Seuls + Retombe Terrasses.